

*SISTEMA DE ILUMINACIÓN
Iluminación interior mediante pastillas de LED en cadena de alto flujo luminoso (1 W/unidad por pastilla)
Letra A: 42w
Letra R: 60w
Letra V: 40w
Letra A: 42w
Letra L: 35w
El logo lleva transformador de 200w

5 transformadores de 60w
Total conjunto 500w



VERSION1

PROYECTO GRAFICO

DISEÑO

Jonathan Seldas

CLIENTE

ARVAL

ELEMENTOS

RÓTULO DE CORONACIÓN

ESCALA


1:60/ A4

FECHA

30.05.2023

PAGINA

1

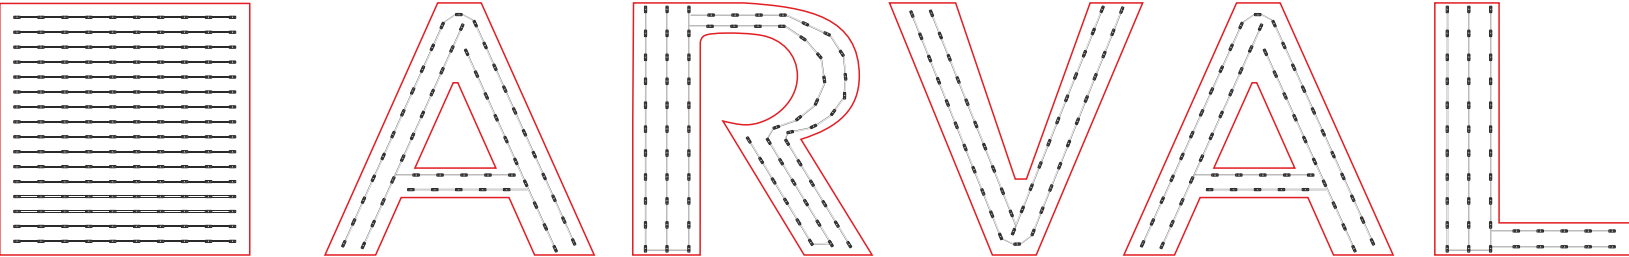

Interruptor crepuscular de montaje en superficie y detección frontal electrónica. Diseñado para el control de alumbrados de pequeñas instalaciones en jardines, parques, viviendas, escaparates, etc...

Dispone de led de conexión/desconexión para facilitar la identificación de estado. Incorpora retardo para evitar actuaciones falsas por destellos luminosos y el margen de ajuste es muy amplio con un valor mínimo muy bajo.

Tensión nominal: 230 Vc.a.
Frecuencia nominal: 50-60 Hz.
Consumo propio: 3,4 VA cap (0,7 W aprox.).
Tipo de contacto simple, con potencial.
Tipo de de sulfuro de Cadmio
Sensibilidad: 5-200 lux lineal.
Temperatura de funcionamiento: -25 °C a +45 °C.
Clase de protección II según EN 60335 en condiciones de montaje correctas.
Tipo de protección IP 55 según EN 60529.
Instalación en superficie o báculo.
Retardo de encendido/desconexión 30 seg. aprox.



 xprinta your GRAPHIC extension	CLIENTE: ARVAL			DIRECCION: C/ ANABEL SEGURA 14, ALCOBENDAS, MADRID			APROBACION CLIENTE		DISEÑO ☐		FABRICACIÓN ☐			
	CONTACTO:			TLF.1:		TLF.2:		E-MAIL:		FECHA: / /			FIRMA:	
	TRABAJO: ROTULO DE CORONACIÓN													

ASOCIADO A

INTERNATIONAL SIGN ASSOCIATION

AVISO LEGAL

El presente diseño / proyecto gráfico pertenece a la propiedad intelectual de XPRINTA SIGNS SPAIN, S.L. con C.I.F. B86679289, por lo que se encuentra debidamente protegido por la ley 22 / 1987 de 11 de noviembre. En consecuencia, el cliente se compromete explícitamente a no hacer uso del mismo sin contar para ello con el consentimiento expreso y por escrito de XPRINTA, renunciando a su propio fuero y sometiéndose a los tribunales de Madrid.

CONTACTO

Laguna del Marquesado, 10 Nave 18 · 28021 Madrid · T. 91 505 29 27 · www.xprinta.com

DESCRIPCIÓN ELEMENTOS

RÓTULO ARVAL

Plano estructura

UBICACIÓN: FACHADA SUR

Detalle agarre entre cercha y soporte letras mediante pletina tipo percha

Incluye estructura en perfil de acero galvanizado compuesta por cerchas en perfil tubular con aplicación de esmalte antioxidante al minio y acabado RAL 9003.

Necesario servicio de alquiler de autogrúa propulsada 60TM para su instalación.

VERSION

1

PROYECTO GRAFICO

DISEÑO



Jonathan Seldas

CLIENTE



ARVAL

ELEMENTOS

RÓTULO DE CORONACIÓN

ESCALA


1:60 / A4

FECHA

30.05.2023

PAGINA

2

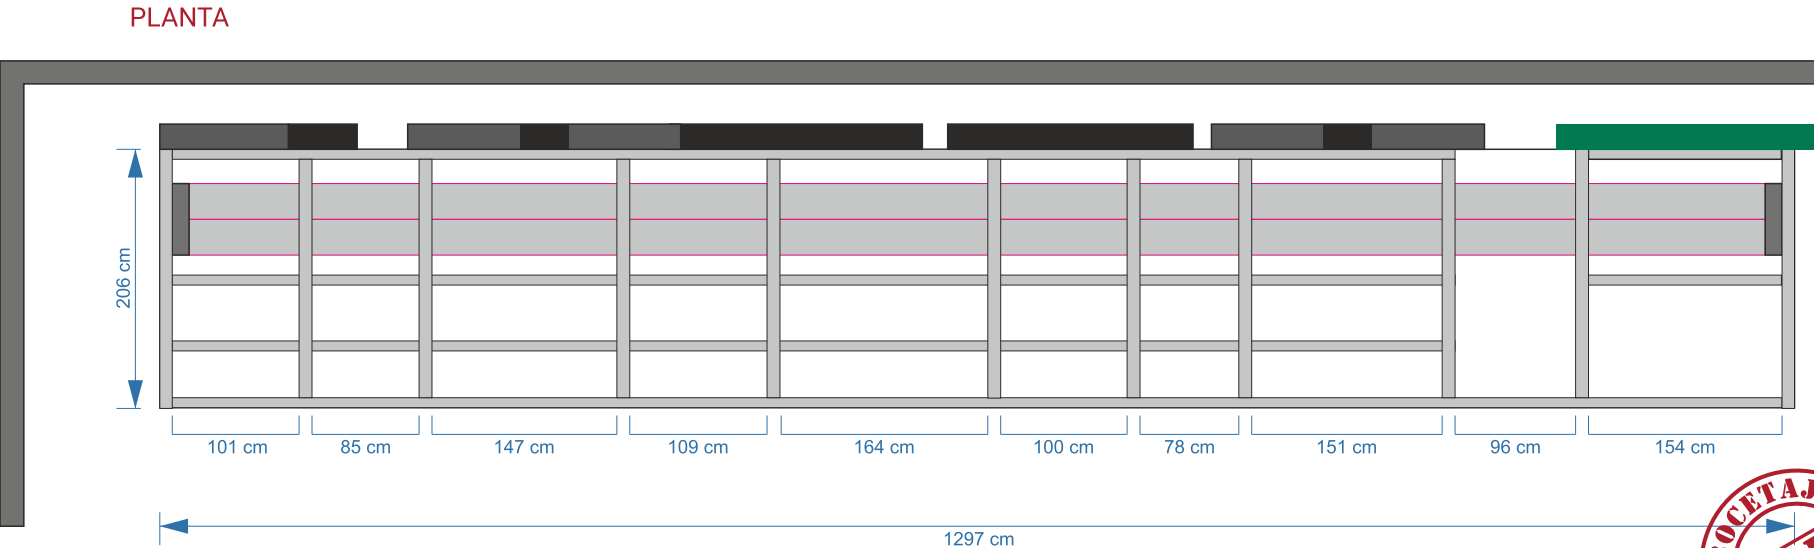

 xprinta your GRAPHIC extension	CLIENTE: ARVAL	DIRECCION: C/ ANABEL SEGURA 14, ALCOBENDAS, MADRID	APROBACION CLIENTE	DISEÑO ☐	FABRICACIÓN ☐
	CONTACTO:	TLF.1: 655718563	TLF.2: E-MAIL: pilar.domingo@flulle.com	FECHA: / /	FIRMA: _____
	TRABAJO: ROTULO DE CORONACIÓN				

ASOCIADO A





INTERNATIONAL SIGN ASSOCIATION

AVISO LEGAL

El presente diseño / proyecto gráfico pertenece a la propiedad intelectual de XPRINTA SIGNS SPAIN, S.L. con C.I.F. B86679289, por lo que se encuentra debidamente protegido por la ley 22 / 1987 de 11 de noviembre. En consecuencia, el cliente se compromete explícitamente a no hacer uso del mismo sin contar para ello con el consentimiento expreso y por escrito de XPRINTA, renunciando a su propio fuero y sometiéndose a los tribunales de Madrid.

CONTACTO

Laguna del Marquesado, 10 Nave 18 · 28021 Madrid · T. 91 505 29 27 · www.xprinta.com



ALZADO Y COTAS

INFO FOTULOS

*** ESTRUCTURA DE LETRAS**
Plancha de aluminio 2 mm de espesor, corte fresadora controlada por ordenador con forma letra y logo "ARVAL". Corte banda perimetral o tizón con cizalla neumática
130-150 mm de ancho. Formado y soldado TIG de banda perimetral. Lijado y repasado. Ángulo frontal de sujeción en aluminio plegado y soldado 25 mm, formado según letra. Anclaje a cuerpo principal de la letra mediante atornillado. Acabado termolacado al polvo con pretratamiento antióxido, presecado a 160°, y horno de polimerizado a 220°, en color RAL similar a Pantone corporativo.

*** FRENTE DE LETRAS**
Plancha de metacrilato Black & White 4 mm espesor, translúcido, corte en fresadora controlada por ordenador con forma letra y "ARVAL". Logo en metacrilato alto impago blanco opal con rotulación en vinilo translúcido

*** SISTEMA DE ILUMINACIÓN**
Iluminación interior mediante pastillas de LED en cadena de alto flujo luminoso (1 W/unidad por pastilla), con placa de aluminio para disipación de calor y tecnología CCT para estabilización de flujo eléctrico. Convertidores adecuados al número de LEDS totales del rótulo.

*** ESTRUCTURA DE SUJECCIÓN**
Realizada mediante pórticos de acero laminado IPE-100, de 384 cm de altura y 205 cm de fondo aproximadamente. La estructura se sustentará mediante placas de 25x25x1 cm y contrapesos de hormigón armado adecuados al cálculo realizado en el proyecto visado ya realizado. Medidas de letras 1297 x 200 cm
Medidas totales con estructura 1297 x 395 cm
Instalación incluida
Medios de izado grúa de 60Tn para izado de materiales y trabajos de instalación, incluidos. Plataforma colocada en vial interno privado que no requiere de permisos municipales de ocupación de vía pública. Conexionado de rótulos a punto de luz existente * Precio estimado hasta confirmación de cálculo de estructura necesaria por parte de arquitecto

Sensor crepuscular para encendido/apagado de rótulo



VERSION

1

PROYECTO GRAFICO

DISEÑO

Jonathan Seldas

CLIENTE

ARVAL

ELEMENTOS

RÓTULO DE CORONACIÓN

ESCALA

1:200 / A4

FECHA

30.05.2023


PAGINA

3

	CLIENTE: ARVAL	DIRECCION: C/ ANABEL SEGURA 14, ALCOBENDAS, MADRID	APROBACION CLIENTE	DISEÑO ☐	FABRICACIÓN ☐
	CONTACTO:	TLF.1:	TLF.2:	E-MAIL:	FECHA:
	TRABAJO: ROTULO DE CORONACIÓN				

RENDER 3D

RÓTULO ARVAL - VISTA TRASERA

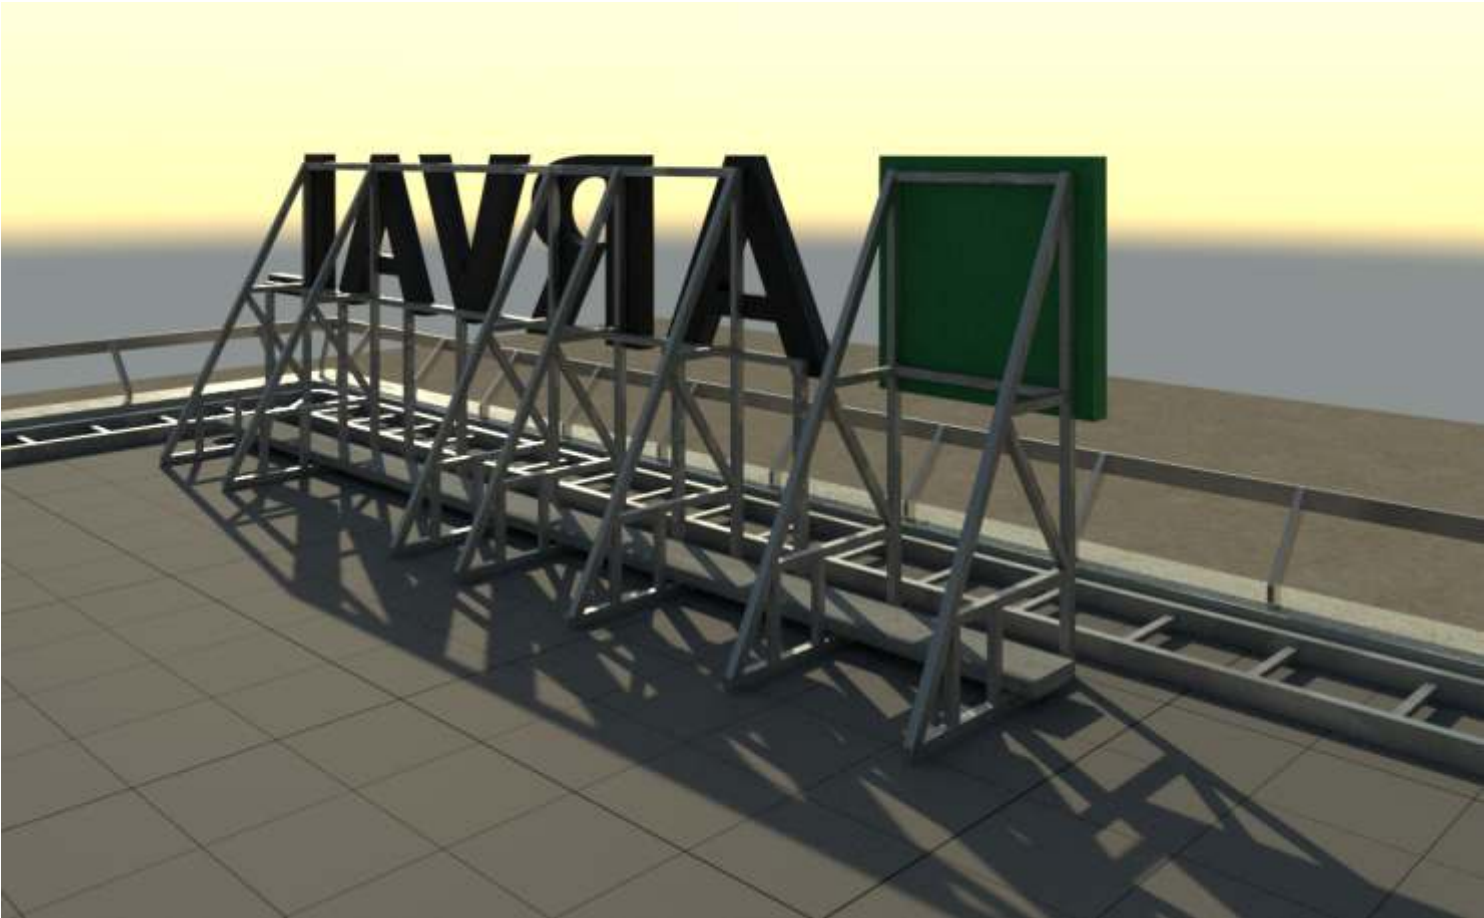

Disponible Modelo de visualización AR:



VERSION

1

PROYECTO

GRAFICO

DISEÑO

Jonathan Seldas

CLIENTE

ARVAL

ELEMENTOS

RÓTULO DE CORONACIÓN

ESCALA

1:150 / A4

FECHA

30.05.2023

PAGINA

4



	CLIENTE: ARVAL	DIRECCION: C/ ANABEL SEGURA 14, ALCOBENDAS, MADRID	APROBACION CLIENTE	DISEÑO ☐	FABRICACIÓN ☐
	CONTACTO:	TLF.1:	TLF.2:	E-MAIL:	FECHA: / / FIRMA:
	TRABAJO: ROTULO DE CORONACIÓN				

 RENDER 3D

RÓTULO ARVAL - SIMULACIÓN NOCTURNA
Luces Black & White



Disponible Modelo
de visualización AR:



VERSION

1

PROYECTO
GRAFICO

DISEÑO



Jonathan Seldas

CLIENTE



ARVAL

ELEMENTOS

RÓTULO DE
CORONACIÓN

ESCALA

1:150 / A4

FECHA

30.05.2023

PAGINA

5



	CLIENTE: ARVAL	DIRECCION: C/ ANABEL SEGURA 14, ALCOBENDAS, MADRID	APROBACION CLIENTE	DISEÑO ☐	FABRICACIÓN ☐
	CONTACTO:	TLF.1:	TLF.2:	E-MAIL:	FECHA: / / FIRMA:
	TRABAJO: ROTULO DE CORONACIÓN				

FOTOMONTAJE

RÓTULO ARVAL - VISTA URBANA 2

La imagen es ilustrativa y sólo a modo de ejemplo, es una aproximación al tamaño y proporción real.



VERSION

1

PROYECTO GRAFICO

DISEÑO

Jonathan Seldas

CLIENTE

ARVAL

ELEMENTOS

RÓTULO DE CORONACIÓN

ESCALA

1:150 / A4

FECHA

30.05.2023

PAGINA

6

	CLIENTE: ARVAL	DIRECCION: C/ ANABEL SEGURA 14, ALCOBENDAS, MADRID	APROBACION CLIENTE	DISEÑO ☐	FABRICACIÓN ☐
	CONTACTO:	TLF.1:	TLF.2:	E-MAIL:	FECHA:
	TRABAJO: ROTULO DE CORONACIÓN				FIRMA: